



VE.06

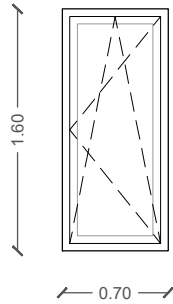


|               |                            |
|---------------|----------------------------|
| Quantity      | 2 uds                      |
| LOCATION      | BAÑOS-PATIO                |
| WINDOW SYSTEM | 1 HOJA OSCILOBATIENTE      |
| GLASS         | VIDRIO 4+4/16(ARGÓN)/4+4mm |
| MATERIALS     | ALUMINIO CON RTP           |
| OBSERVATIONS  | RAL A DEFINIR POR DF       |

VE.03

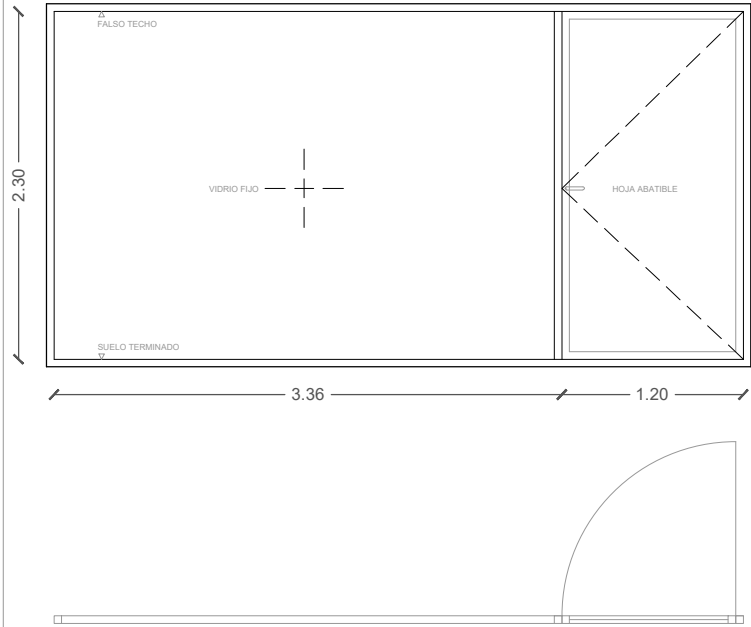


|               |                                 |
|---------------|---------------------------------|
| Quantity      | 1 ud                            |
| LOCATION      | PATIO                           |
| WINDOW SYSTEM | FIJO+PUERTA ABATIBLE CON UMBRAL |
| GLASS         | VIDRIO 6+6/16(ARGÓN)/4+4mm      |
| MATERIALS     | ALUMINIO CON RTP                |
| OBSERVATIONS  | RAL A DEFINIR POR DF            |

VE.04

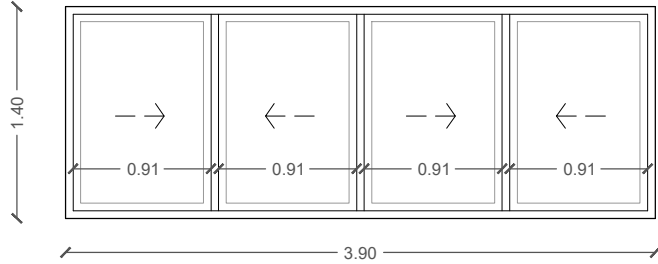


|               |                            |
|---------------|----------------------------|
| Quantity      | 1 ud                       |
| LOCATION      | COCINA-PATIO               |
| WINDOW SYSTEM | VENTANAS CORREDERAS        |
| GLASS         | VIDRIO 4+4/16(ARGÓN)/4+4mm |
| MATERIALS     | ALUMINIO CON RTP           |
| OBSERVATIONS  | RAL A DEFINIR POR DF       |

VE.05

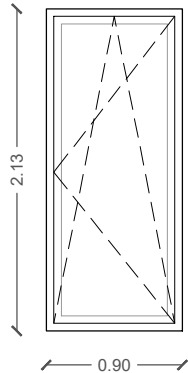

|               |                            |
|---------------|----------------------------|
| Quantity      | 7 uds                      |
| LOCATION      | FACHADA Y PATIO INTERIOR   |
| WINDOW SYSTEM | 2 HOJAS OSCILOBATIENTES    |
| GLASS         | VIDRIO 4+4/16(ARGÓN)/4+4mm |
| MATERIALS     | ALUMINIO CON RTP           |
| OBSERVATIONS  | RAL A DEFINIR POR DF       |

VE.02

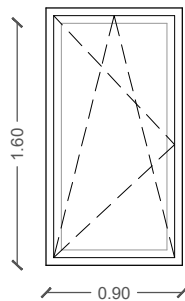

|               |                            |
|---------------|----------------------------|
| Quantity      | 2 uds                      |
| LOCATION      | FACHADA                    |
| WINDOW SYSTEM | 2 HOJAS OSCILOBATIENTES    |
| GLASS         | VIDRIO 4+4/16(ARGÓN)/4+4mm |
| MATERIALS     | ALUMINIO CON RTP           |
| OBSERVATIONS  | RAL A DEFINIR POR DF       |



TERRETA studio  
Sergi Ibáñez Cantavella  
Colegiado COACV 15.232

PROYECTO BÁSICO DE REFORMA  
GENERAL DE VIVIENDA UNIFAMILIAR  
ENTRE MEDIANERAS

Situación: Calle Marqués de Cáceres, 18, 46183, l'Eliana

Promotor: Laura Espinosa Aloy

Plano: **CARPINTERIA EXTERIOR**

Escala: 1/50 Cotas expresadas en metros. Fecha: Mayo 2025

Nº: **P.2.5.1**