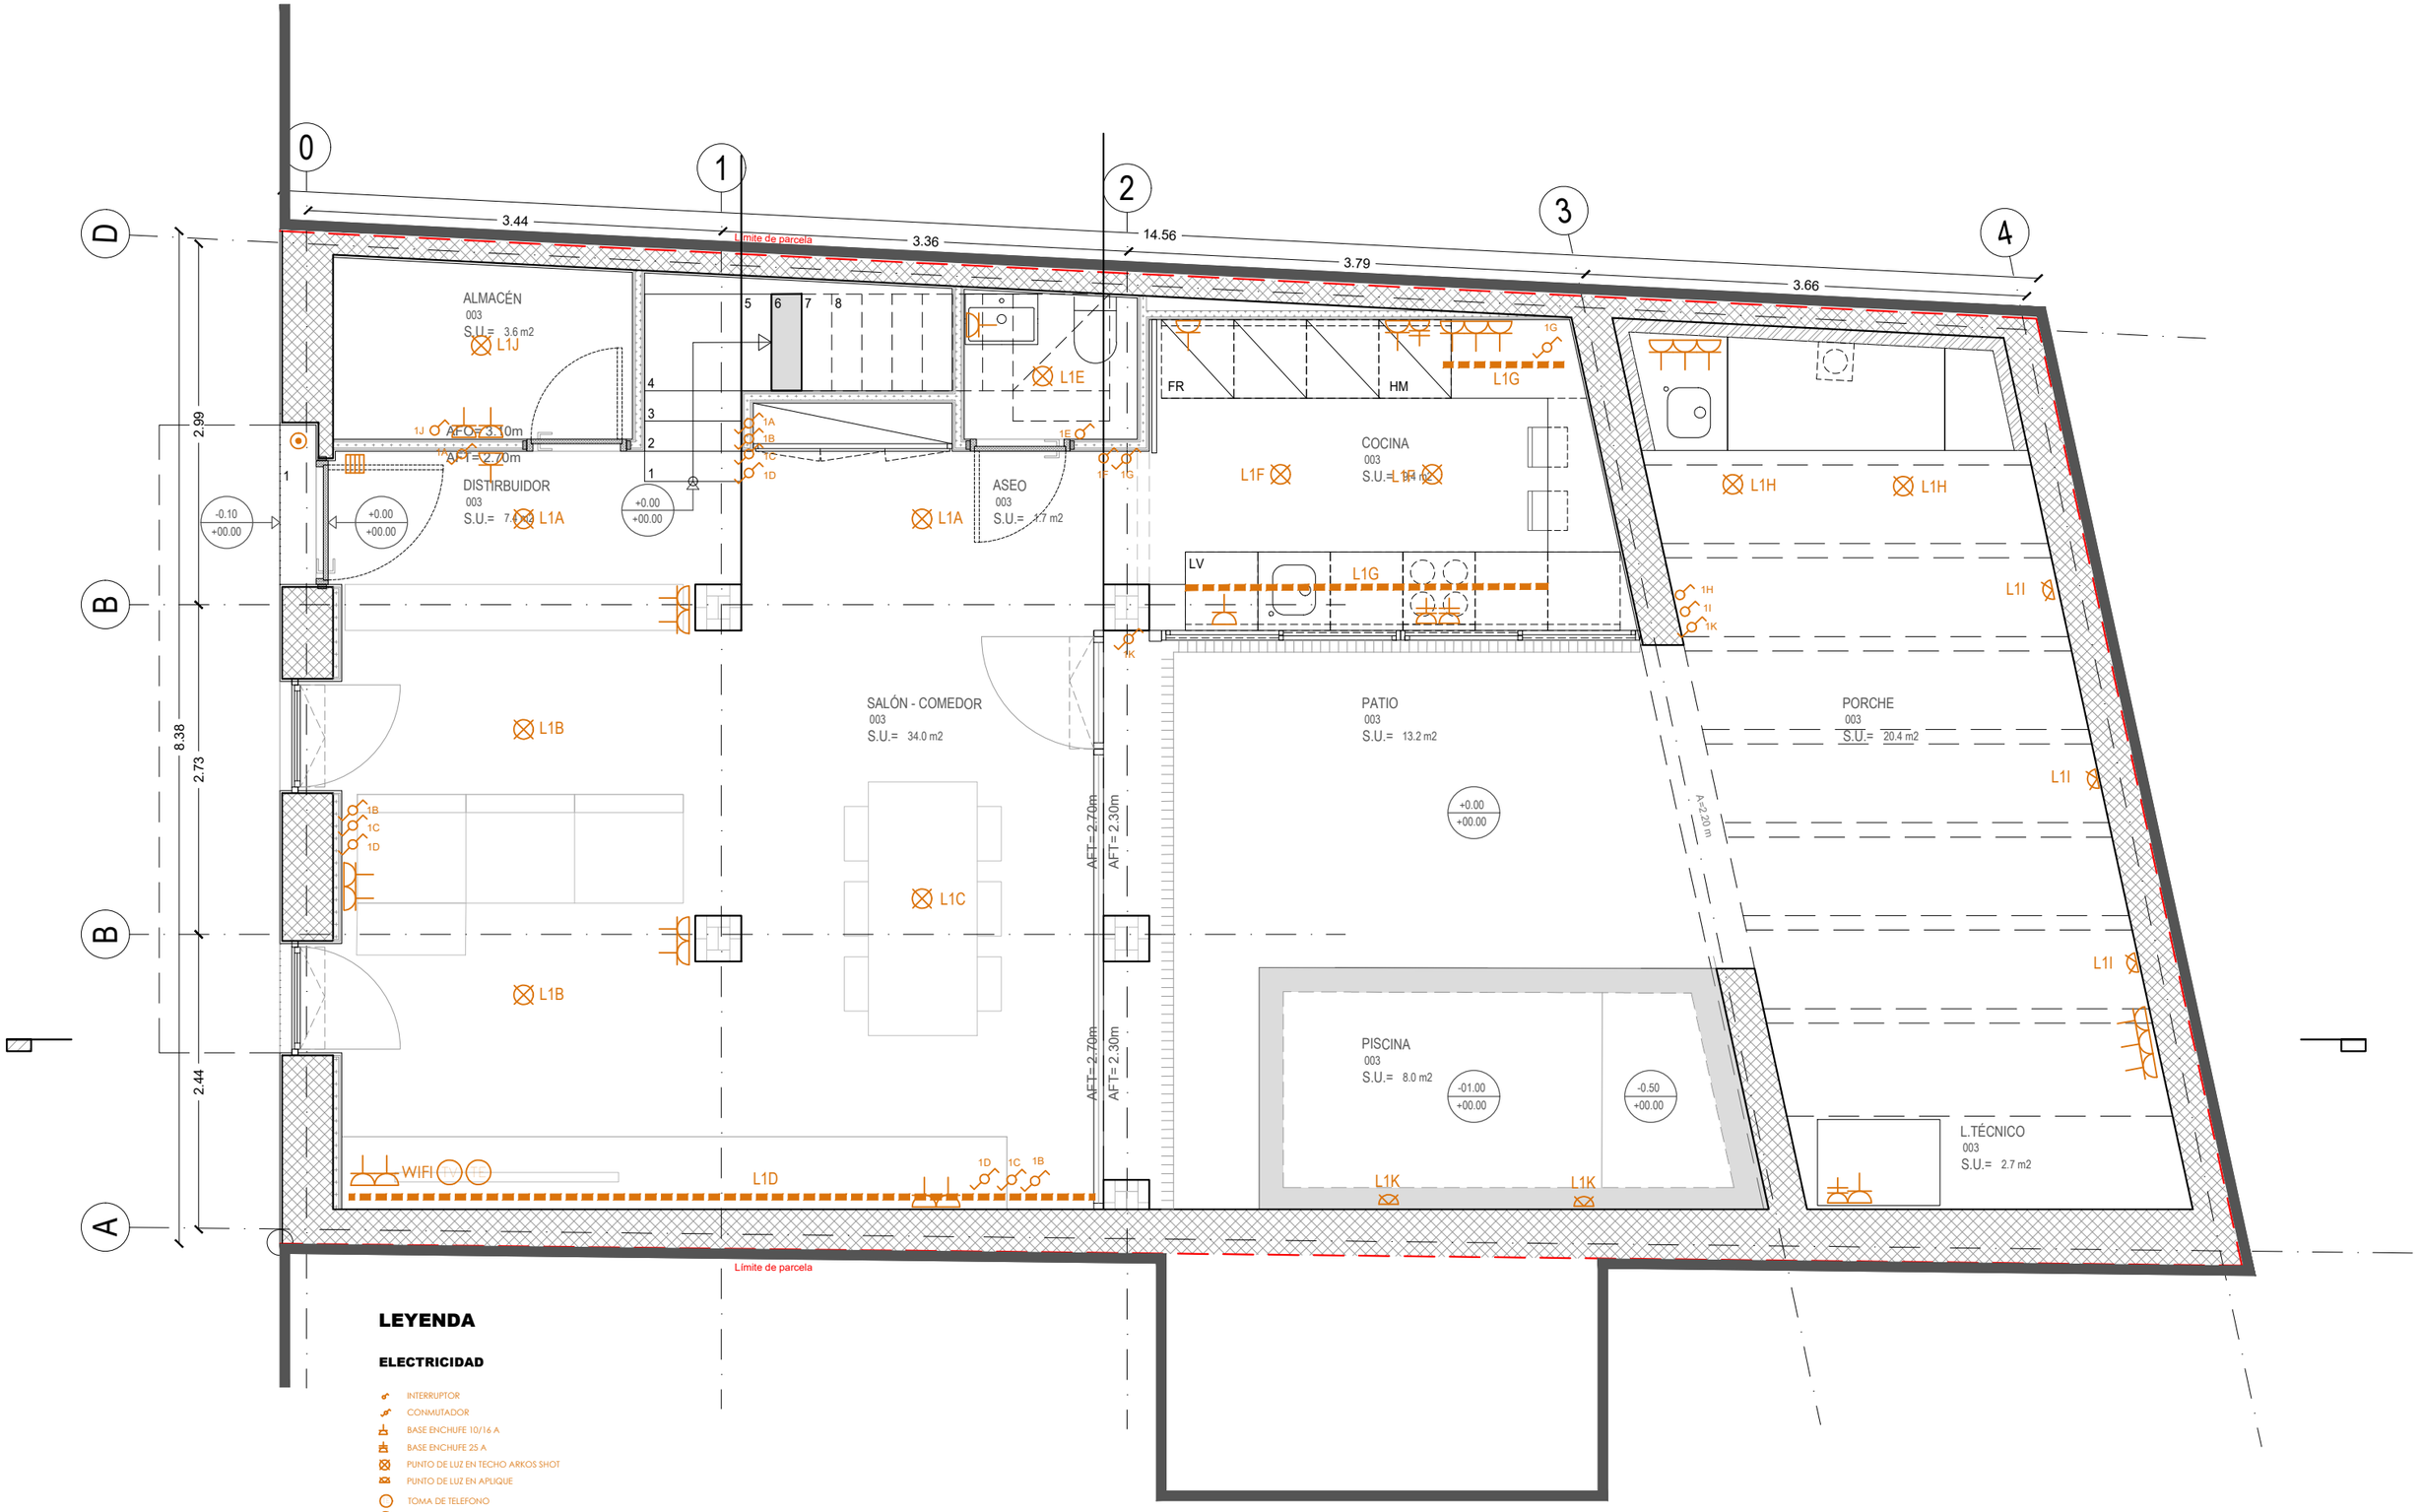


LEYENDA

ELECTRICIDAD

- INTERRUPTOR
- CONMUTADOR
- BASE ENCHUFE 10/16 A
- BASE ENCHUFE 25 A
- PUNTO DE LUZ EN TECHO ARKOS SHOT
- PUNTO DE LUZ EN APLIQUE
- TOMA DE TELEFONO
- TOMA DE TELEVISION
- EXTRACTOR DE HUMOS
- VIDEO PORTERO - PANTALLA DOMÓTICA
- TIMBRE
- ZUMBADOR
- CUADRO GENERAL
- WIFI CONEXION WIFI